



1. РАМА (вид сверху) — ЗАД ← | → ПЕРЕД

поперечин 40×20: 5 шт + 3 под швы пола | кронштейны рессор: 8 шт | аморти: 4 шт | крылья: 4 шт | аморти. балки: +10 и +100 см
профиль: 60×60×2 | ось: 50×50×4 | рессоры: 5-лист. ×4
центр. балка + косынки (4 шт)
М6 пол→перемычки: 42 шт (шаг ~350 мм)
Дышло 80×40×3: центр.луч 120 см, боковые 200 см → 1 м от рамы

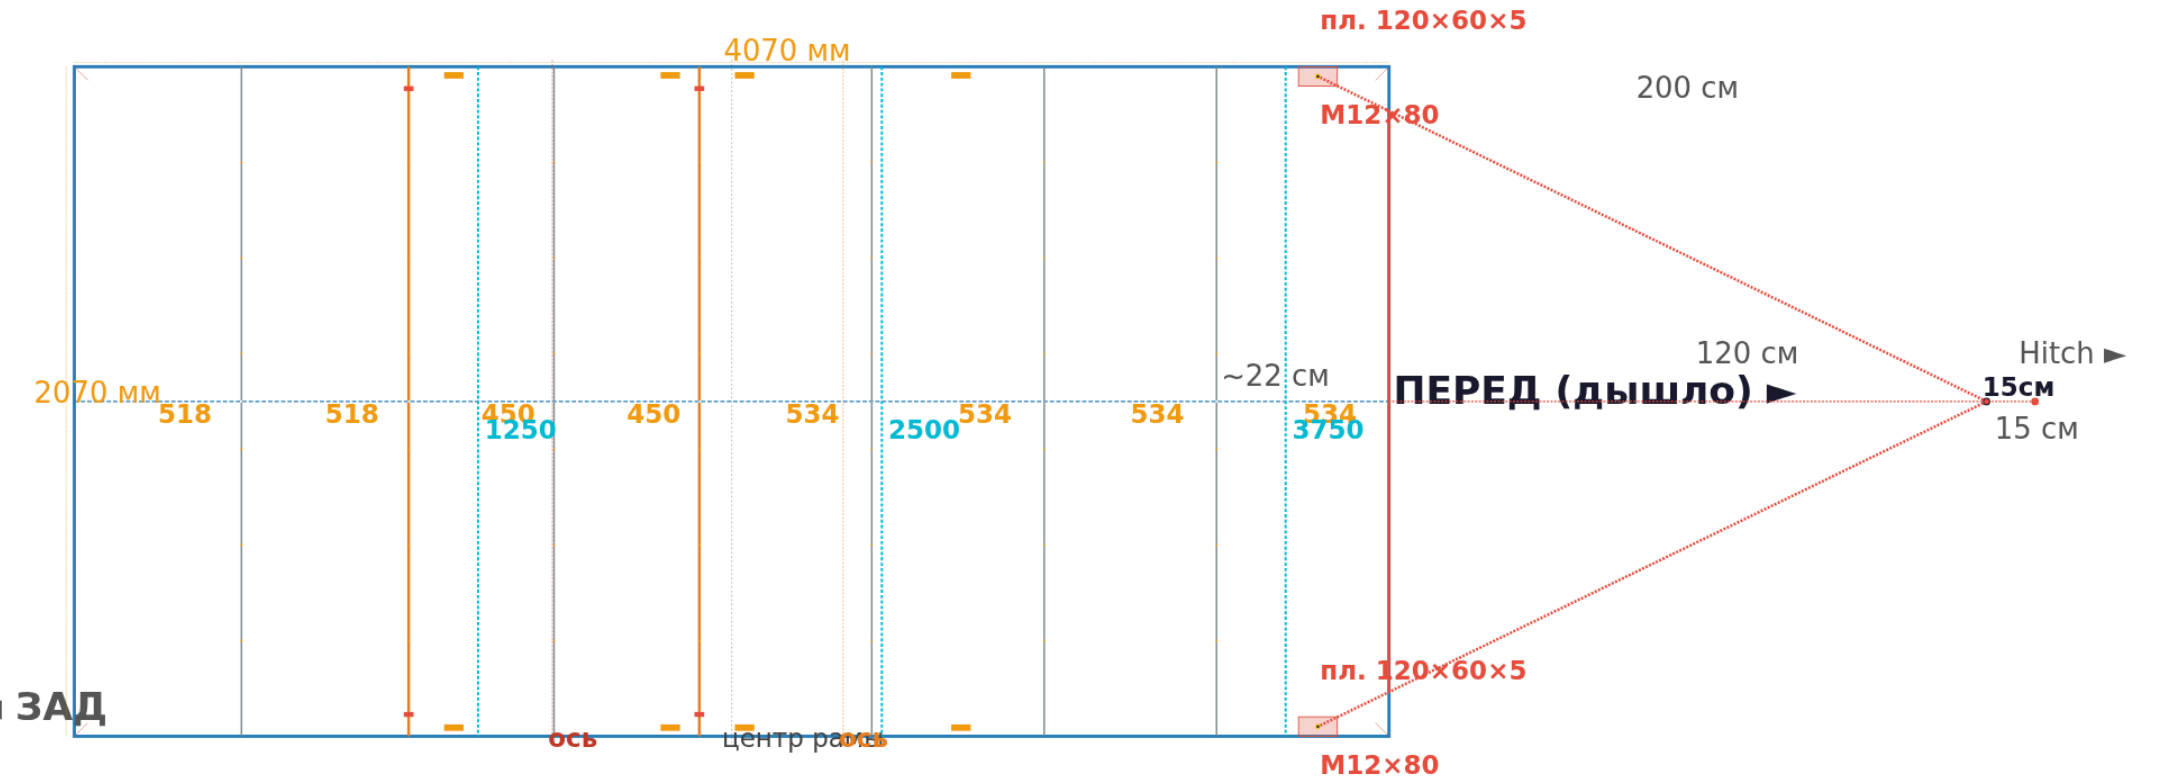


2. БОРТА (длинный и короткий)

Длинный борт (×2): 4 перемычек, шаг ~814 мм
Короткий борт (×2): 2 перемычек, шаг ~690 мм
Всего перемычек: 12 шт | профиль 25×25×2 | метраж 3.6 м
М8 борт→рама: 10 шт (шаг ~800, отступ 250)

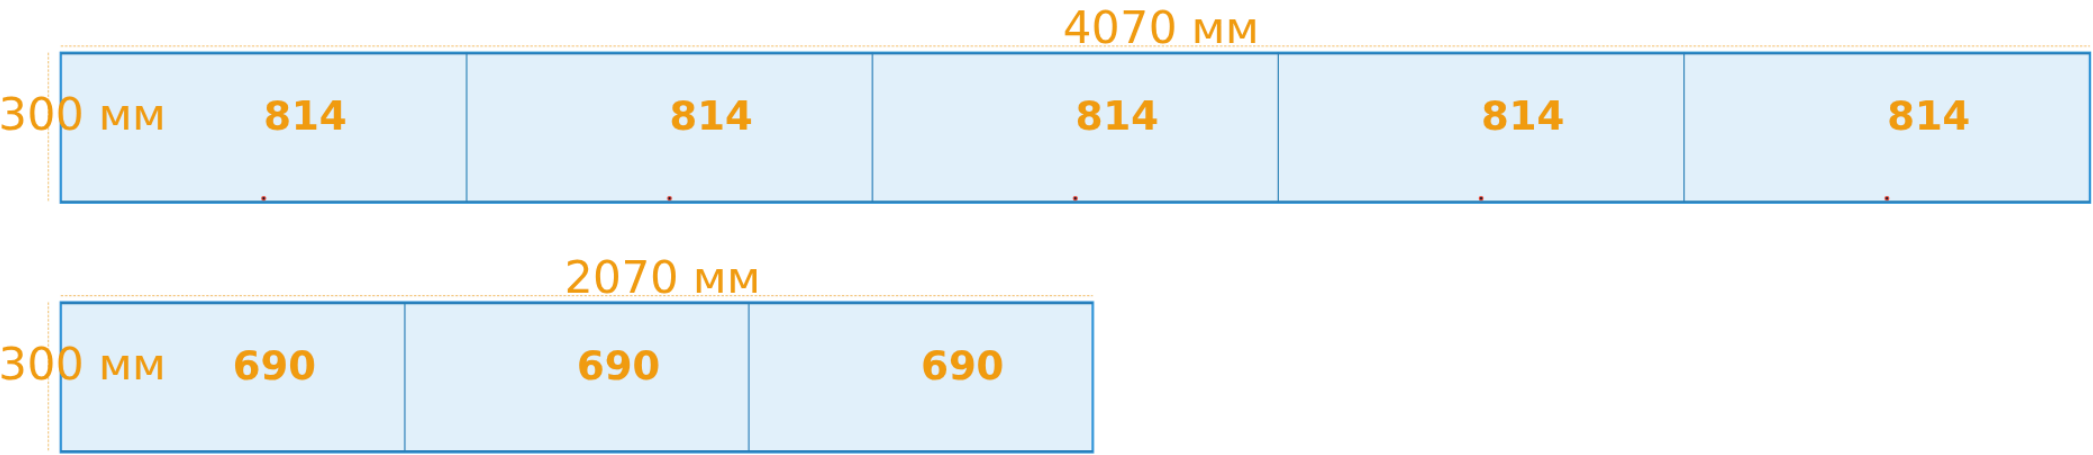

3. КАРКАС ТЕНТА (вид сбоку)

Бок. рамки (×2): 20×20×1.5, высота 300+1700=2000 мм | стоек = дуг: 7 шт
Дуги (П-обр.): 7 шт, 20×20×1.5, концы 100 мм → проставки 25×25×2×100
Аэро скос: передняя стойка -300 мм, верхняя труба наклонная 800 мм
М6 каркас→борта: 10 шт (шаг ~800 мм)

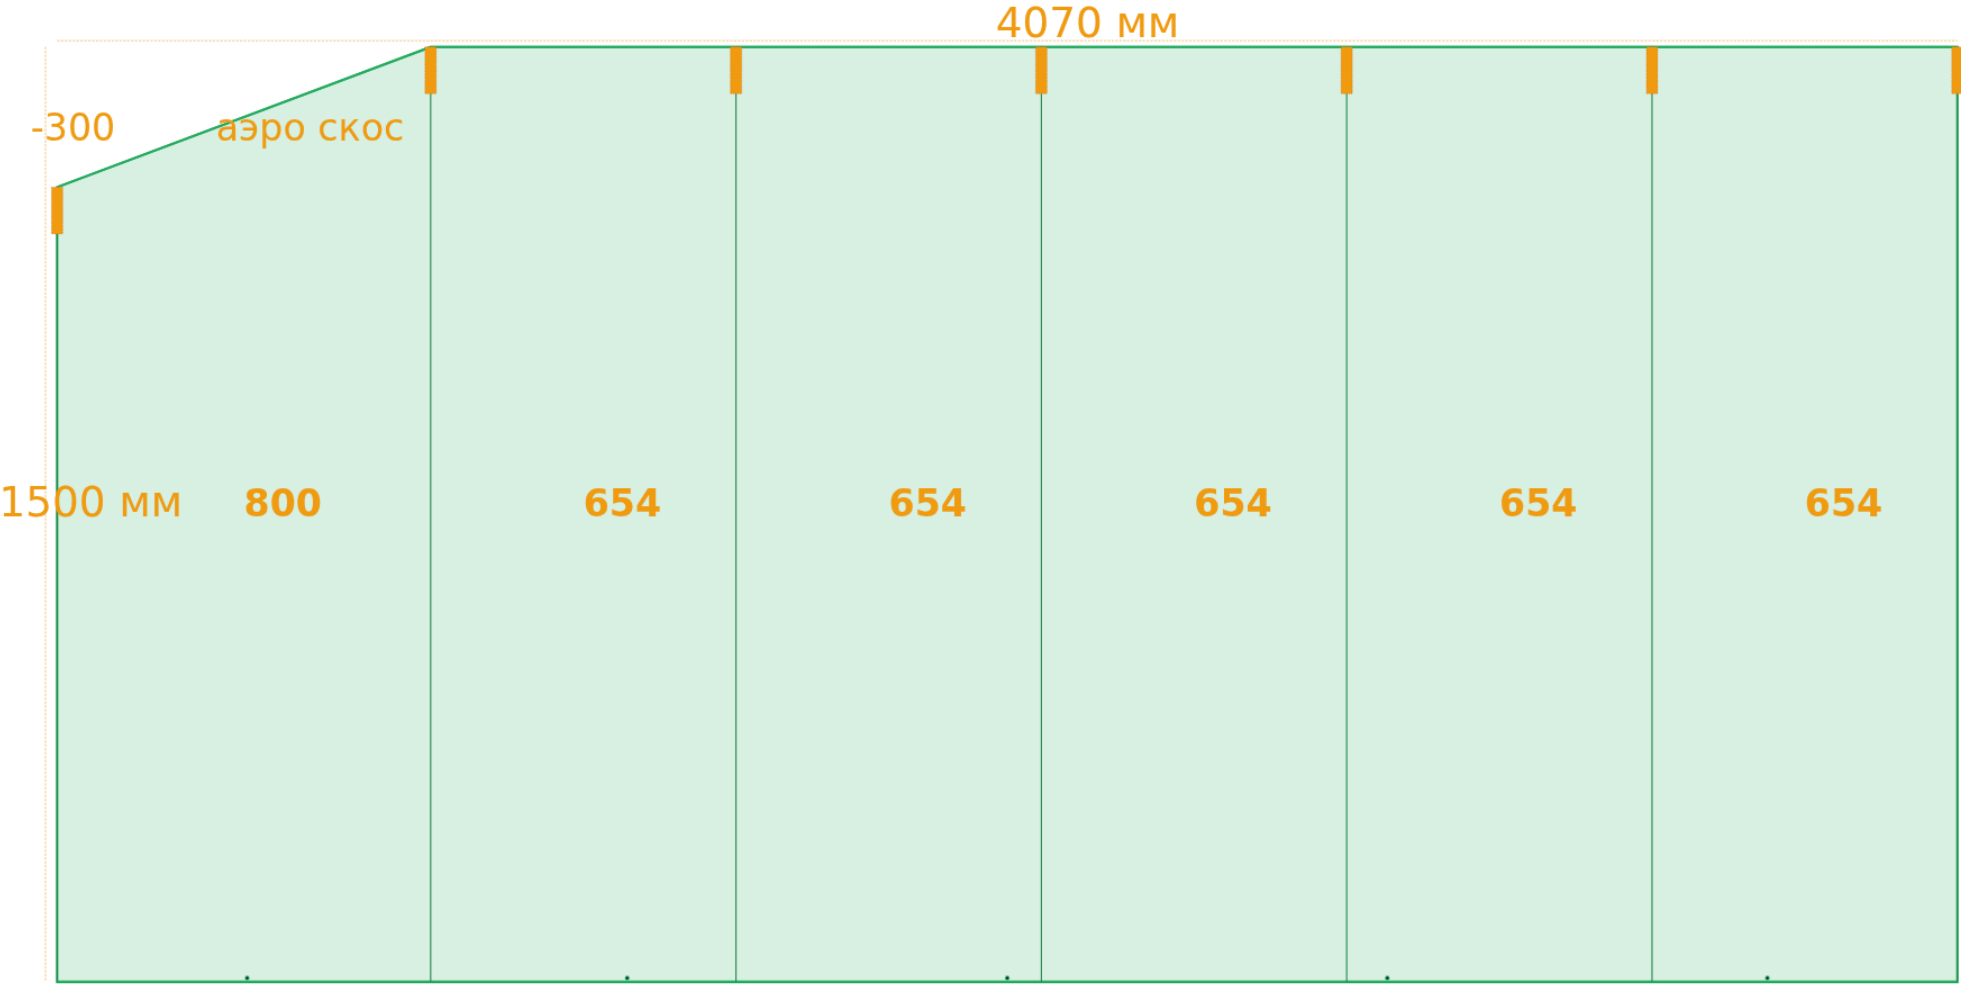


ООО Самбарс · прицепы

Самбарс 2.00×4.0 м

Масштаб 1:10 · Лист 3 из 5

4. ВИД СЗАДИ (тент + борт + рама + задняя рамка)

Задняя рамка: 2 стойки 180 мм + перемычка 2070 мм = 2.43 м (40×20×2)
Пластина номера 400×180×1 | подфарники 2×П-обр. 180×200×140×1
Ось 50×50×4 | Рессоры 5-лист. ×4
Дуга П-обр. 20×20×1.5, концы 100 мм
тент 170 см | 2000 мм (заявл.) | 2070 мм (рама)

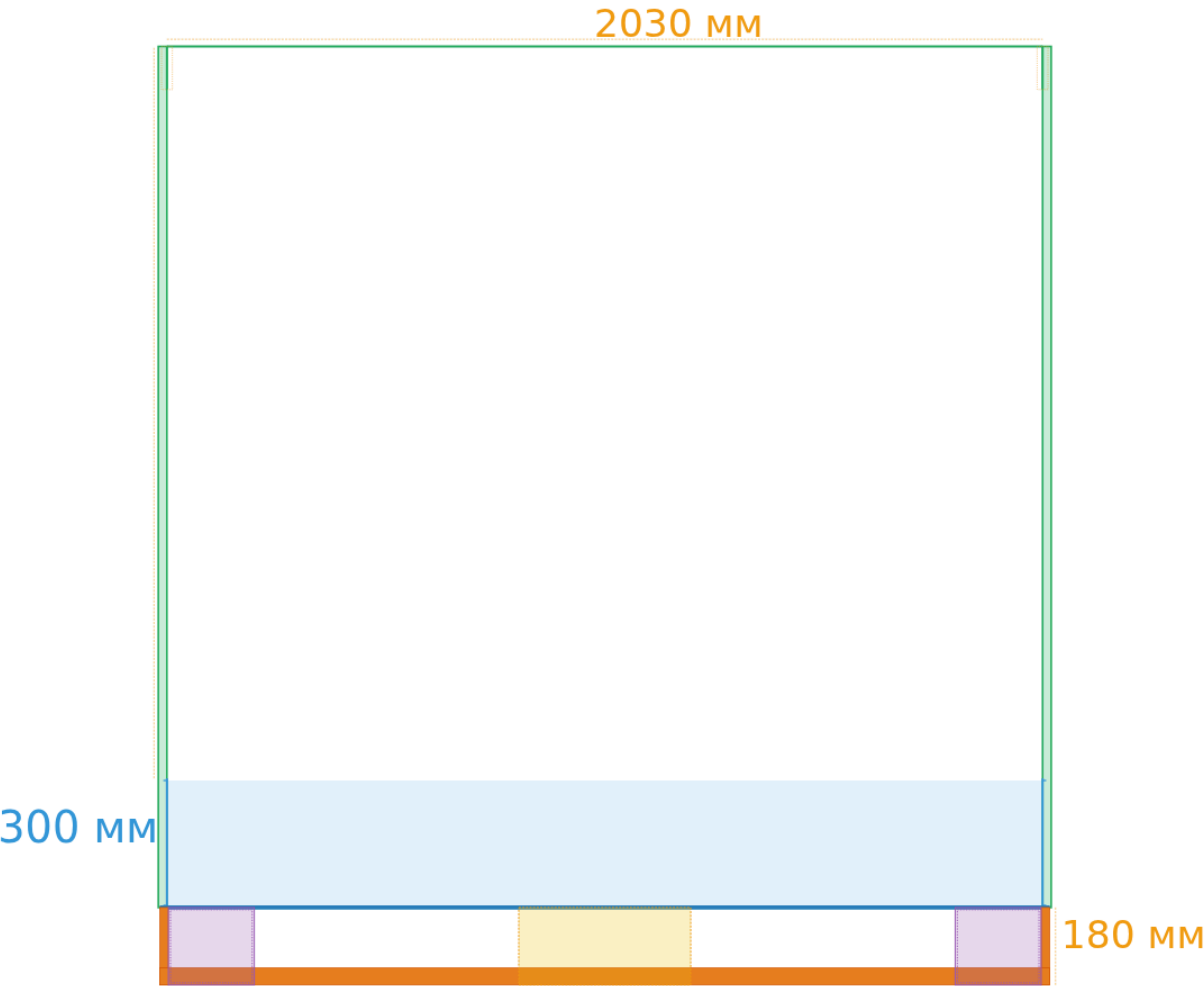

5. ТЕНТ (раскрой)

Тент ПВХ 650 г/м2, раскрой: ширина полотна 5910 мм (высота 5470 мм + 2х220 подгиб) → 3 полос(ы) по 1970 мм из рулона 2500 мм

Аэро скос: передний клапан ниже на 300 мм

Люверсы d10 (шаг 300, отступ 50) | усилители на сгибах 200 мм

000 Самбарс · прицепы

Самбарс 2.00×4.0 м

Масштаб 1:20 · Лист 5 из 5